南京晓庄学院方山校区校园总体规划总平面引导图(2021)

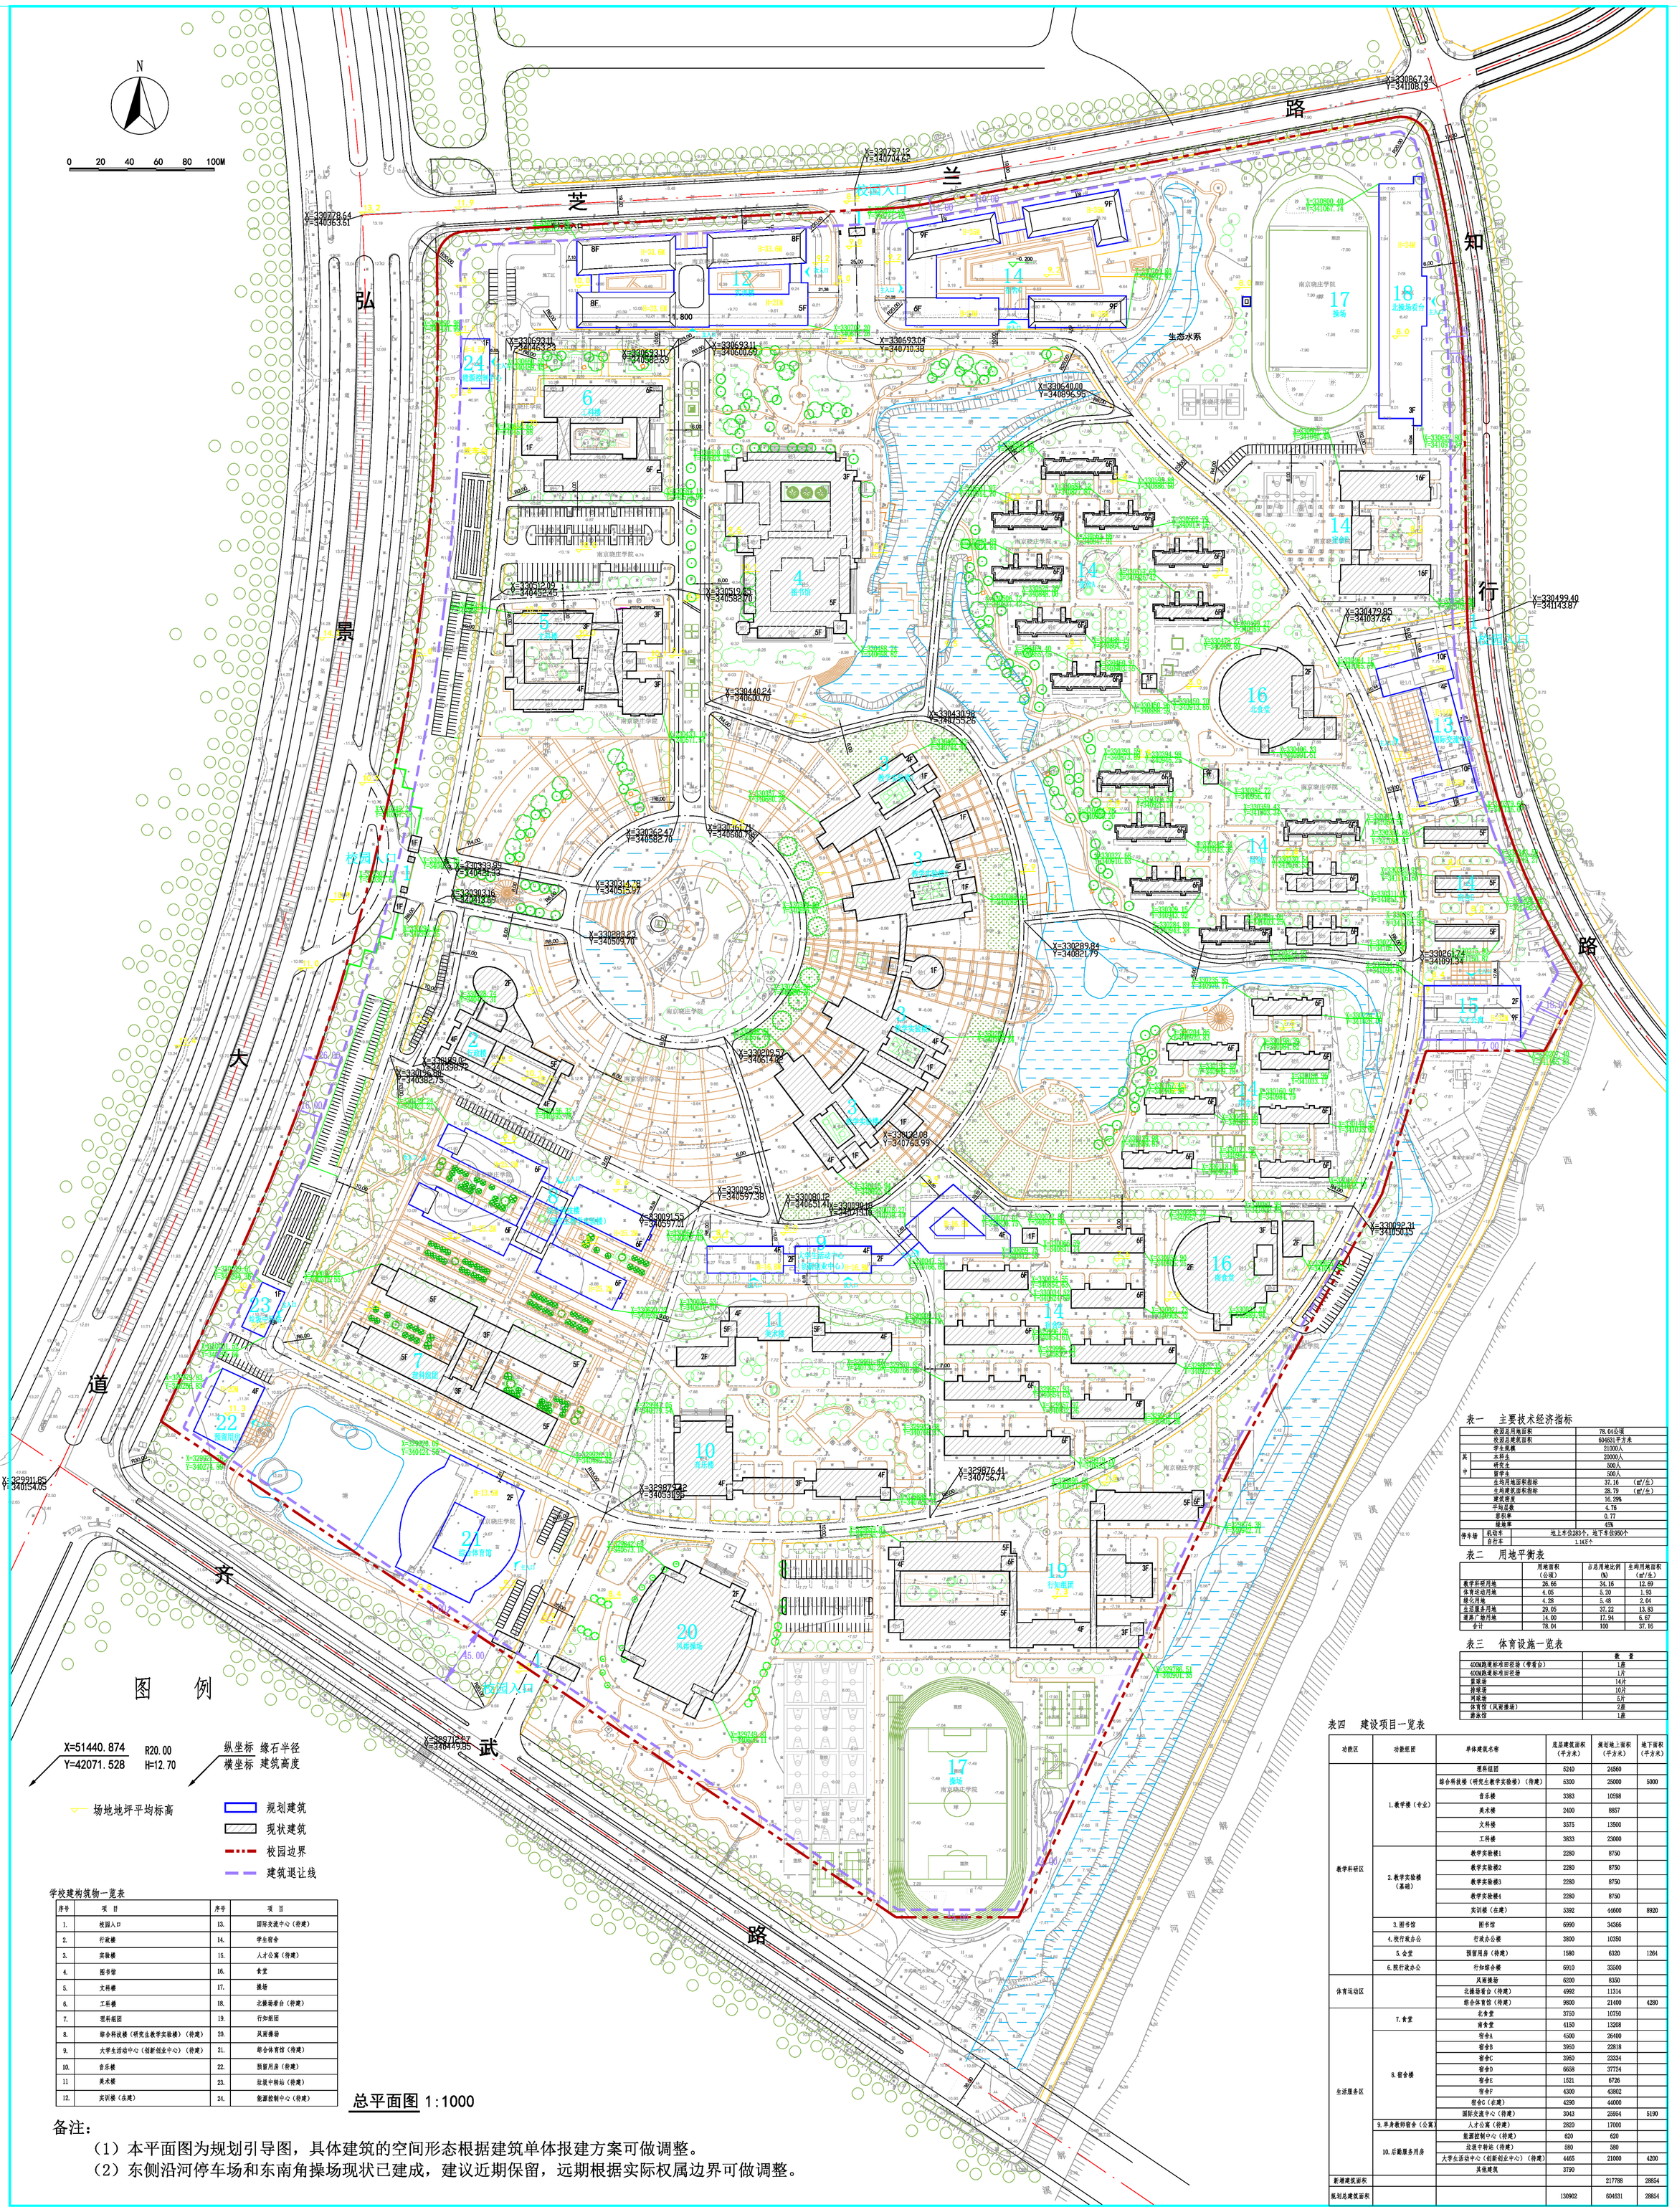

学校建构筑物一览表

序号	项 目	序号	项 目
1.	校园入口	13.	国际交流中心（待建）
2.	行政楼	14.	学生宿舍
3.	实验楼	15.	人才公寓（待建）
4.	图书馆	16.	食堂
5.	文科楼	17.	操场
6.	工科楼	18.	北操场看台（待建）
7.	理科组团	19.	行知组团
8.	综合科技楼（研究生教学实验楼）（待建）	20.	风雨操场
9.	大学生活动中心（创新创业中心）（待建）	21.	综合体育馆（待建）
10.	音乐楼	22.	预留用房（待建）
11	美术楼	23.	垃圾中转站（待建）
12.	实训楼（在建）	24.	能源控制中心（待建）

总平面图 1:1000

表一 主要技术经济指标

校园总用地面积		78.04公顷
校园总建筑面积		604631平方米
学生规模		21000人
其中	本科生	20000人
	研究生	500人
	留学生	500人
生均用地面积指标		37.16 (㎡/生)
生均建筑面积指标		28.79 (㎡/生)
建筑密度		16.29%
平均层数		4.76
容积率		0.77
绿地率		45%
停车场	机动车	地上车位283个，地下车位950个
	自行车	1.1万个

表二 用地平衡表

	用地面积（公顷）	占总用地比例（%）	生均用地面积（㎡/生）
教学科研用地	26.66	34.16	12.69
体育运动用地	4.05	5.20	1.93
绿化用地	4.28	5.48	2.04
生活服务用地	29.05	37.22	13.83
道路广场用地	14.00	17.94	6.67
合计	78.04	100	37.16

表三 体育设施一览表

	数 量
400M跑道标准田径场（带看台）	1座
400M跑道标准田径场	1片
篮球场	14片
排球场	10片
网球场	5片
体育馆（风雨操场）	2座
游泳馆	1座

表四 建设项目一览表

功能区	功能组团	单体建筑名称	底层建筑面积（平方米）	规划地上面积（平方米）	地下面积（平方米）
教学科研区	1.教学楼（专业）	理科组团	5240	24560	
		综合科技楼（研究生教学实验楼）（待建）	5300	25000	5000
		音乐楼	3383	10598	
		美术楼	2400	8857	
		文科楼	3575	13500	
		工科楼	3833	23000	
	2.教学实验楼（基础）	教学实验楼1	2280	8750	
		教学实验楼2	2280	8750	
		教学实验楼3	2280	8750	
		教学实验楼4	2280	8750	
		实训楼（在建）	5392	44600	8920
	3. 图书馆	图书馆	6990	34366	
	4. 校行政办公	行政办公楼	3800	10350	
	5. 会堂	预留用房（待建）	1580	6320	1264
	6. 院行政办公	行知综合楼	6910	33500	
体育运动区		风雨操场	6200	8350	
		北操场看台（待建）	4992	11314	
		综合体育馆（待建）	9800	21400	4280
生活服务区	7. 食堂	北食堂	3750	10750	
		南食堂	4150	13208	
	8. 留学楼	宿舍A	4500	26400	
		宿舍B	3950	22818	
		宿舍C	3950	23334	
		宿舍D	6658	37724	
		宿舍E	1521	6726	
		宿舍F	4300	43802	
		宿舍G（在建）	4290	44000	
		国际交流中心（待建）	3043	35954	5190
	9. 单身教师宿舍（公寓）	人才公寓（待建）	2820	17000	
	10. 后勤服务用房	能源控制中心（待建）	620	620	
		垃圾中转站（待建）	580	580	
		大学生活动中心（创新创业中心）（待建）	4465	21000	4200
		其他建筑	3790		
新增建筑面积				217788	28854
规划总建筑面积			130902	604631	28854

备注：

（1）本平面图为规划引导图，具体建筑的空间形态根据建筑单体报建方案可做调整。

（2）东侧沿河停车场和东南角操场现状已建成，建议近期保留，远期根据实际权属边界可做调整。